


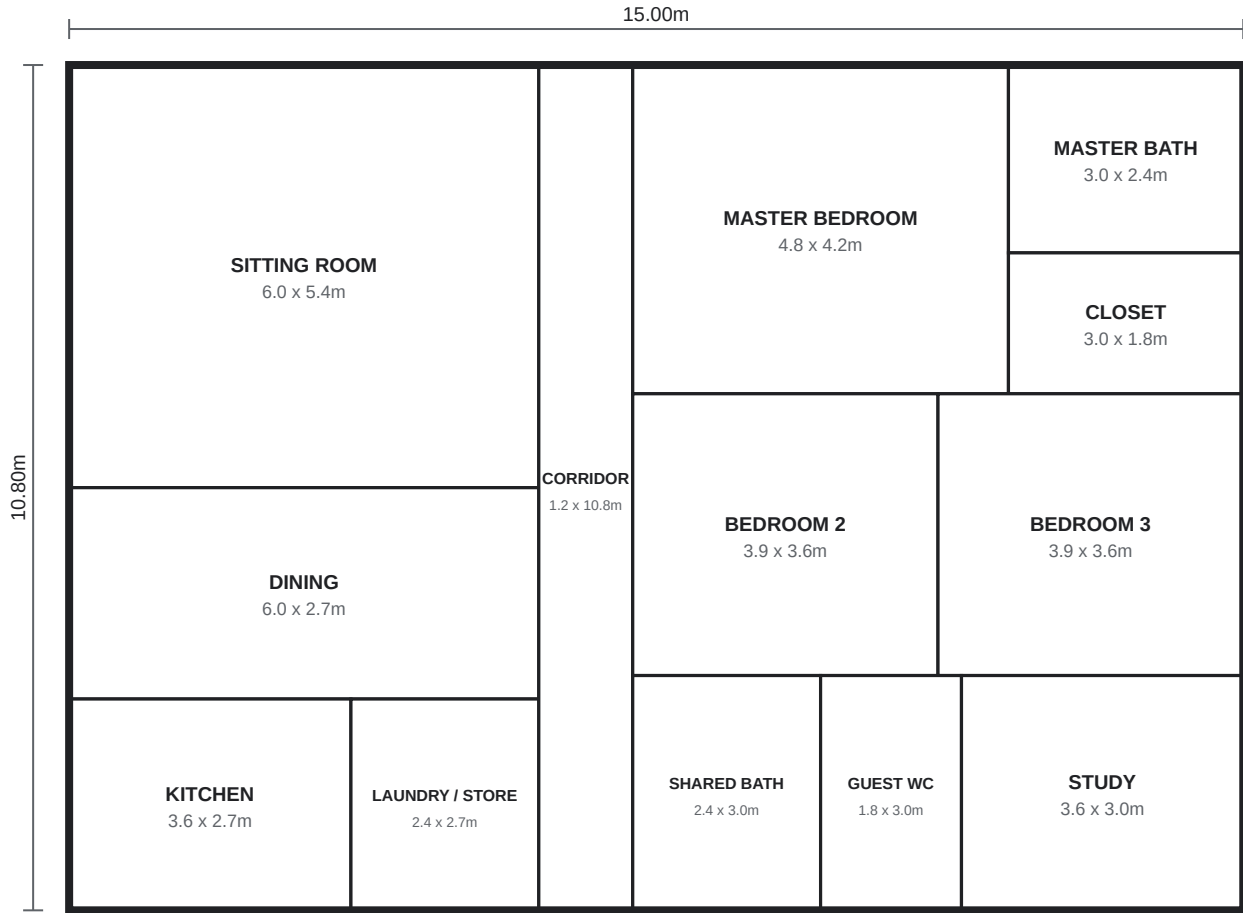

GROUND FLOOR PLAN SCALE 1:100

GENERAL NOTES AND SPECIFICATION

- Foundation: strip footing 750mm wide x 225mm thick, 1:3:6 concrete, base at 1.0m below ground. 5 courses of 9 inch blocks filled with concrete below DPC.
- Ground floor: 150mm oversite concrete 1:2:4 with A142 mesh on 1000 gauge DPM on compacted laterite filling, 600mm average depth.
- Walls: 9 inch sandcrete blocks to external walls, 6 inch to internal walls, 3.0m high. Lintel 225 x 225mm all round, 4 no. 12mm rods, 10mm links at 200mm.
- Columns: 225 x 225mm, 18 no., 4 no. 12mm rods, 10mm links at 200mm.
- Roof: hipped roof, hardwood 2x4 inch rafters and 2x6 inch purlins and wall plate, long-span aluminium 0.55mm, 600mm overhang. Fascia 1x12 inch.
- Finishes: 60x60cm porcelain tiles to all floors, ceramic wall tiles to bathrooms full height 2.4m and kitchen splash 1.2m. PVC ceiling to all rooms. Emulsion internally, textured paint externally, gloss to doors.
- Services: 3 WC, 3 basins, 2 showers, 1 kitchen sink, 2 no. 2000L tanks. 24 light points, 22 double sockets, 1 distribution board.

DOOR SCHEDULE

- D1 Steel security door 1.2 x 2.1m: 2 no.
- D2 Hardwood panel door 0.9 x 2.1m: 9 no.

WINDOW SCHEDULE

- W1 Aluminium sliding window 1.2 x 1.2m: 12 no.
- W2 Louvre window 0.6 x 0.6m: 4 no.

All dimensions in metres unless stated. Do not scale. Contractor to verify on site.

Ibrahim Musa Architects
REGISTERED WITH ARCON

PROJECT
Three Bedroom Bungalow

SITE
Plot 2207, Sector F, Lugbe, Abuja FCT

CLIENT
Dr Aisha Bello

DRAWING
Ground floor plan

DRAWING NO.
KS-02/A-101

SCALE
1:100 at A3

ARCHITECT
Ibrahim Musa, MNIA

STATUS
For pricing

