


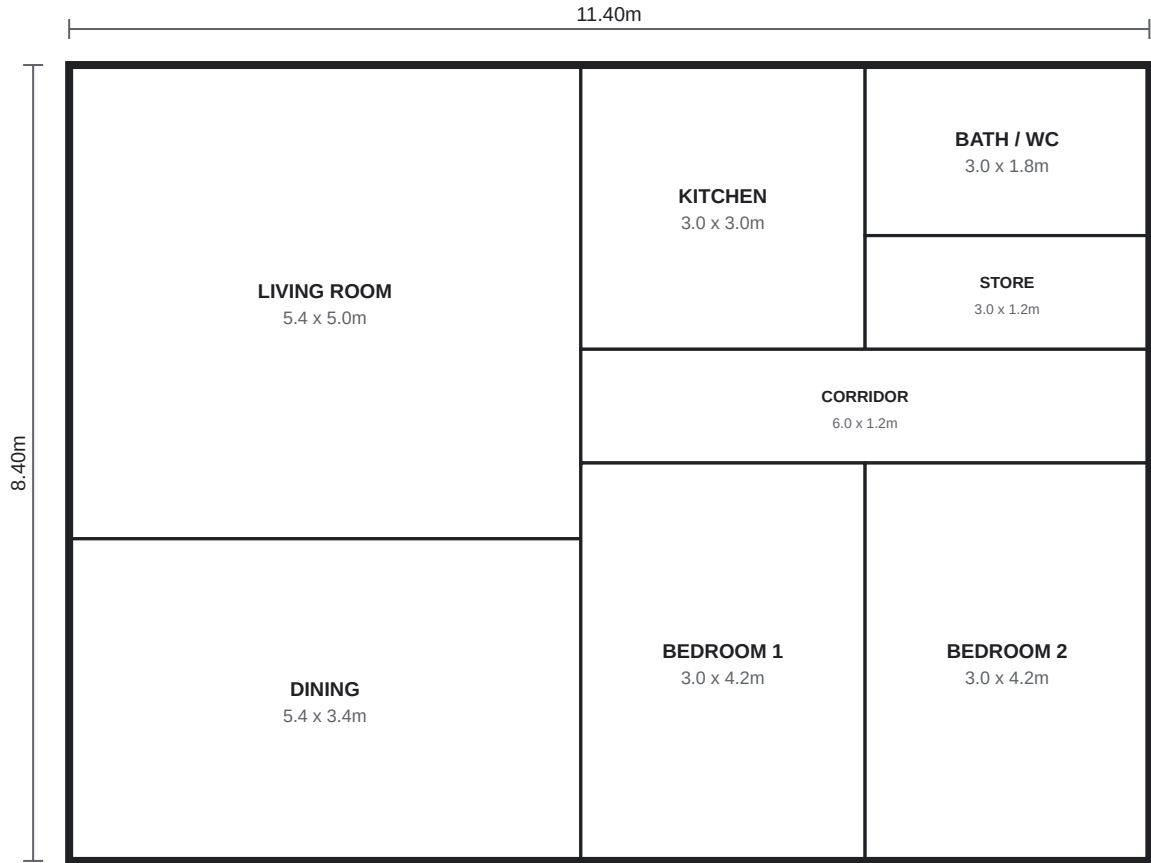

GROUND FLOOR PLAN SCALE 1:100

GENERAL NOTES AND SPECIFICATION

- Foundation: strip footing 675mm wide x 225mm thick, 1:3:6 concrete, base at 900mm below ground. 4 courses of 9 inch blocks filled with concrete below DPC.
- Ground floor: 150mm oversite concrete 1:2:4 on 1000 gauge DPM on compacted laterite filling, 450mm average depth.
- Walls: 9 inch sandcrete blocks to external walls, 6 inch to internal walls, 3.0m high, 1:6 mortar. Lintel 225 x 225mm all round with 4 no. 12mm rods and 10mm links at 200mm.
- Columns: 225 x 225mm at corners and wall junctions (12 no.), 4 no. 12mm rods, 10mm links at 200mm.
- Roof: hipped roof, 2x4 inch hardwood rafters at 600mm, 2x6 inch wall plate, long-span aluminium 0.55mm, 600mm overhang.
- Finishes: 60x60cm porcelain tiles to all floors, ceramic wall tiles to bath and kitchen to 1.8m. Cement render 1:4 both faces. PVC ceiling throughout. Emulsion paint internally, textured paint externally.
- Services: 1 WC, 1 basin, 1 shower, 1 kitchen sink, 2000L overhead tank. 14 light points, 12 double sockets, 1 distribution board.

DOOR SCHEDULE

- D1 Steel security door 1.2 x 2.1m: 2 no.
- D2 Hardwood panel door 0.9 x 2.1m: 4 no.

WINDOW SCHEDULE

- W1 Aluminium sliding window 1.2 x 1.2m: 7 no.
- W2 Louvre window 0.6 x 0.6m (bath): 1 no.

All dimensions in metres unless stated. Do not scale. Contractor to verify on site.

Adebayo Lawal Architects
REGISTERED WITH ARCON

PROJECT
Two Bedroom Bungalow

SITE
Plot 14, Agric Road, Ikorodu, Lagos State

CLIENT
Mr and Mrs Babatunde Ogunleye

DRAWING
Ground floor plan

DRAWING NO.
KS-01/A-101

SCALE
1:100 at A3

ARCHITECT
Adebayo Lawal, MNIA

STATUS
For pricing

