


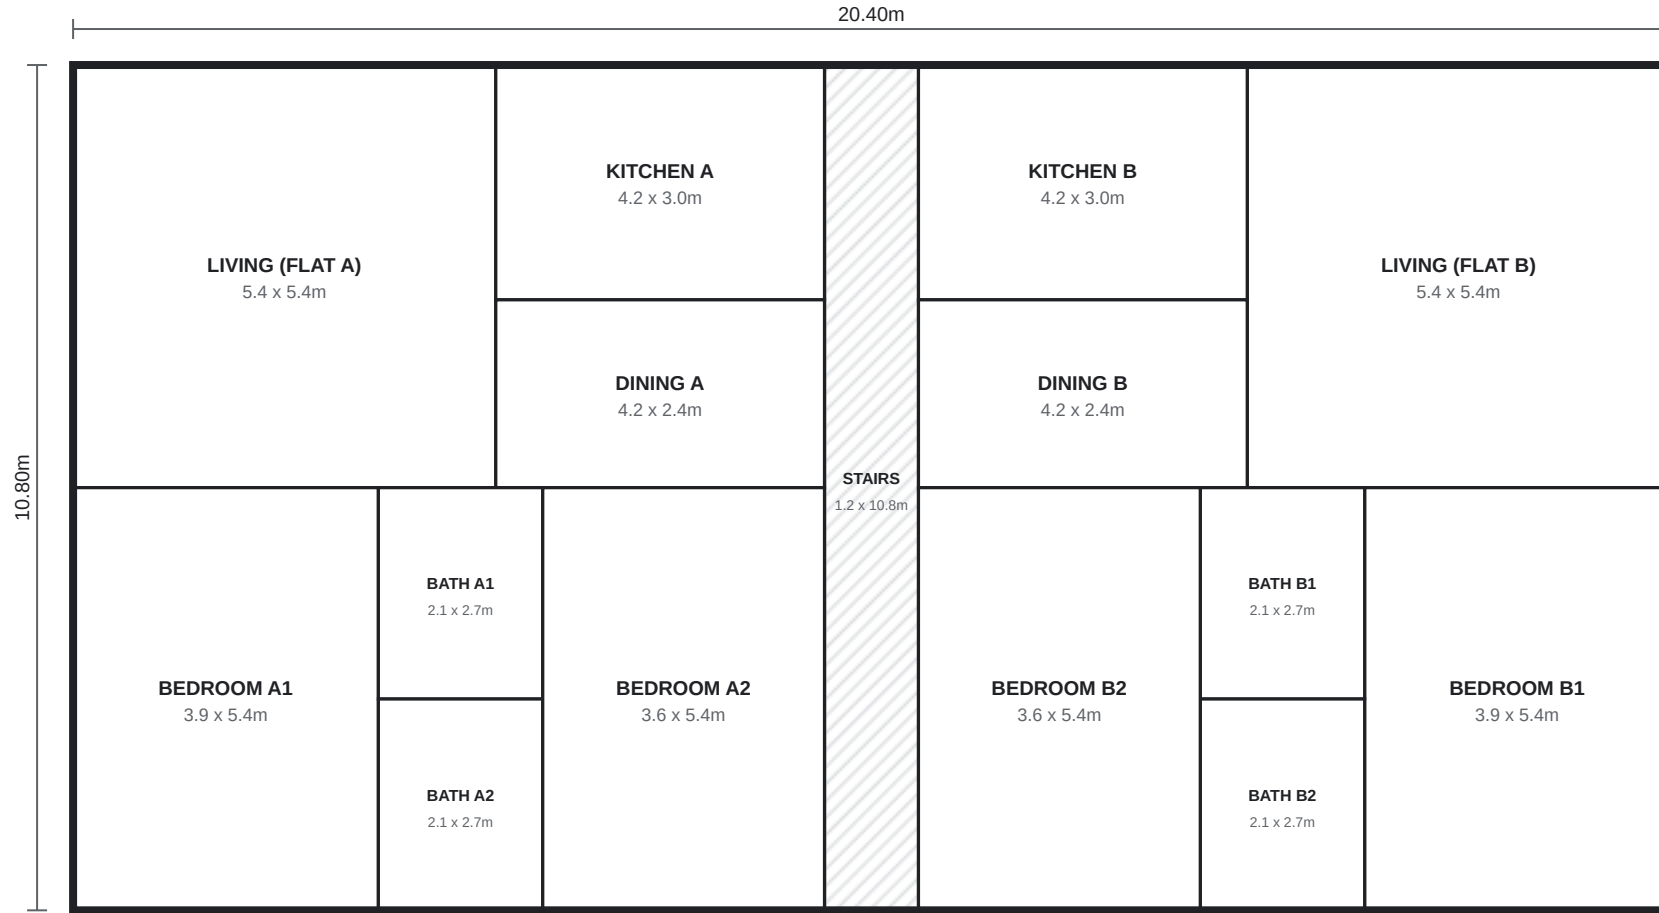

TYPICAL FLOOR PLAN (GROUND AND FIRST FLOOR IDENTICAL) SCALE 1:100

GENERAL NOTES AND SPECIFICATION

- Building: ground floor plus first floor, footprint 20.4 x 10.8m, 2 flats per floor, 4 flats in total. Floor to floor 3.0m.
- Foundation: reinforced strip footing 900mm wide x 250mm, 1:2:4 concrete, 12mm rods, base at 1.2m (soft soil). 6 courses of 9 inch blocks filled with concrete below DPC.
- Ground floor: 150mm oversite concrete on DPM on 900mm laterite filling (waterlogged site).
- Frame: 225 x 225mm columns, 28 no. per floor, 4 no. 16mm rods, 10mm links at 150mm. Beams 225 x 450mm, 4 no. 16mm rods.
- First floor: 150mm suspended slab over the full footprint, 12mm rods at 150mm both ways. Concrete staircase.
- Walls: 9 inch blocks external and party wall, 6 inch internal. Roof: hipped, long-span aluminium 0.55mm on hardwood 2x4 and 2x6 inch members.
- Finishes per flat: porcelain floor tiles throughout, wall tiles to baths and kitchen, PVC ceiling, emulsion inside, textured paint outside.
- Services per flat: 2 WC, 2 basins, 2 showers, 1 kitchen sink. Shared 4 no. 2000L tanks. Per flat 16 light points, 14 double sockets, 1 distribution board.

DOOR SCHEDULE

- D1 Steel security door 1.0 x 2.1m: 8 no. (2 per flat)
- D2 Hardwood panel door 0.9 x 2.1m: 20 no. (5 per flat)

WINDOW SCHEDULE

- W1 Aluminium sliding window 1.2 x 1.2m: 32 no. (8 per flat)
- W2 Louvre window 0.6 x 0.6m: 8 no.

All dimensions in metres unless stated. Do not scale. Contractor to verify on site.

Ebiere Dappa Architects
REGISTERED WITH ARCON

PROJECT
Block of Four 2-Bedroom Flats

SITE
No. 7 Okporo Road, Rumuokoro, Port Harcourt,
Rivers State

CLIENT
Chief Tamuno Briggs

DRAWING
Typical floor plan (ground and first floor identical)

DRAWING NO.
KS-04/A-101

SCALE
1:100 at A3

ARCHITECT
Ebiere Dappa, MNIA

STATUS
For pricing

